

PROJECT INFORMATION


CUSTOMER NAME : Mangomist Resort

PLANT CAPACITY : 237.4kWp

237.4kWp (DC) Photovoltaic system

Consisting of 654 Waaree modules

CONDUIT LAYOUT OF 526 PANELS ON THE SHEET ROOF

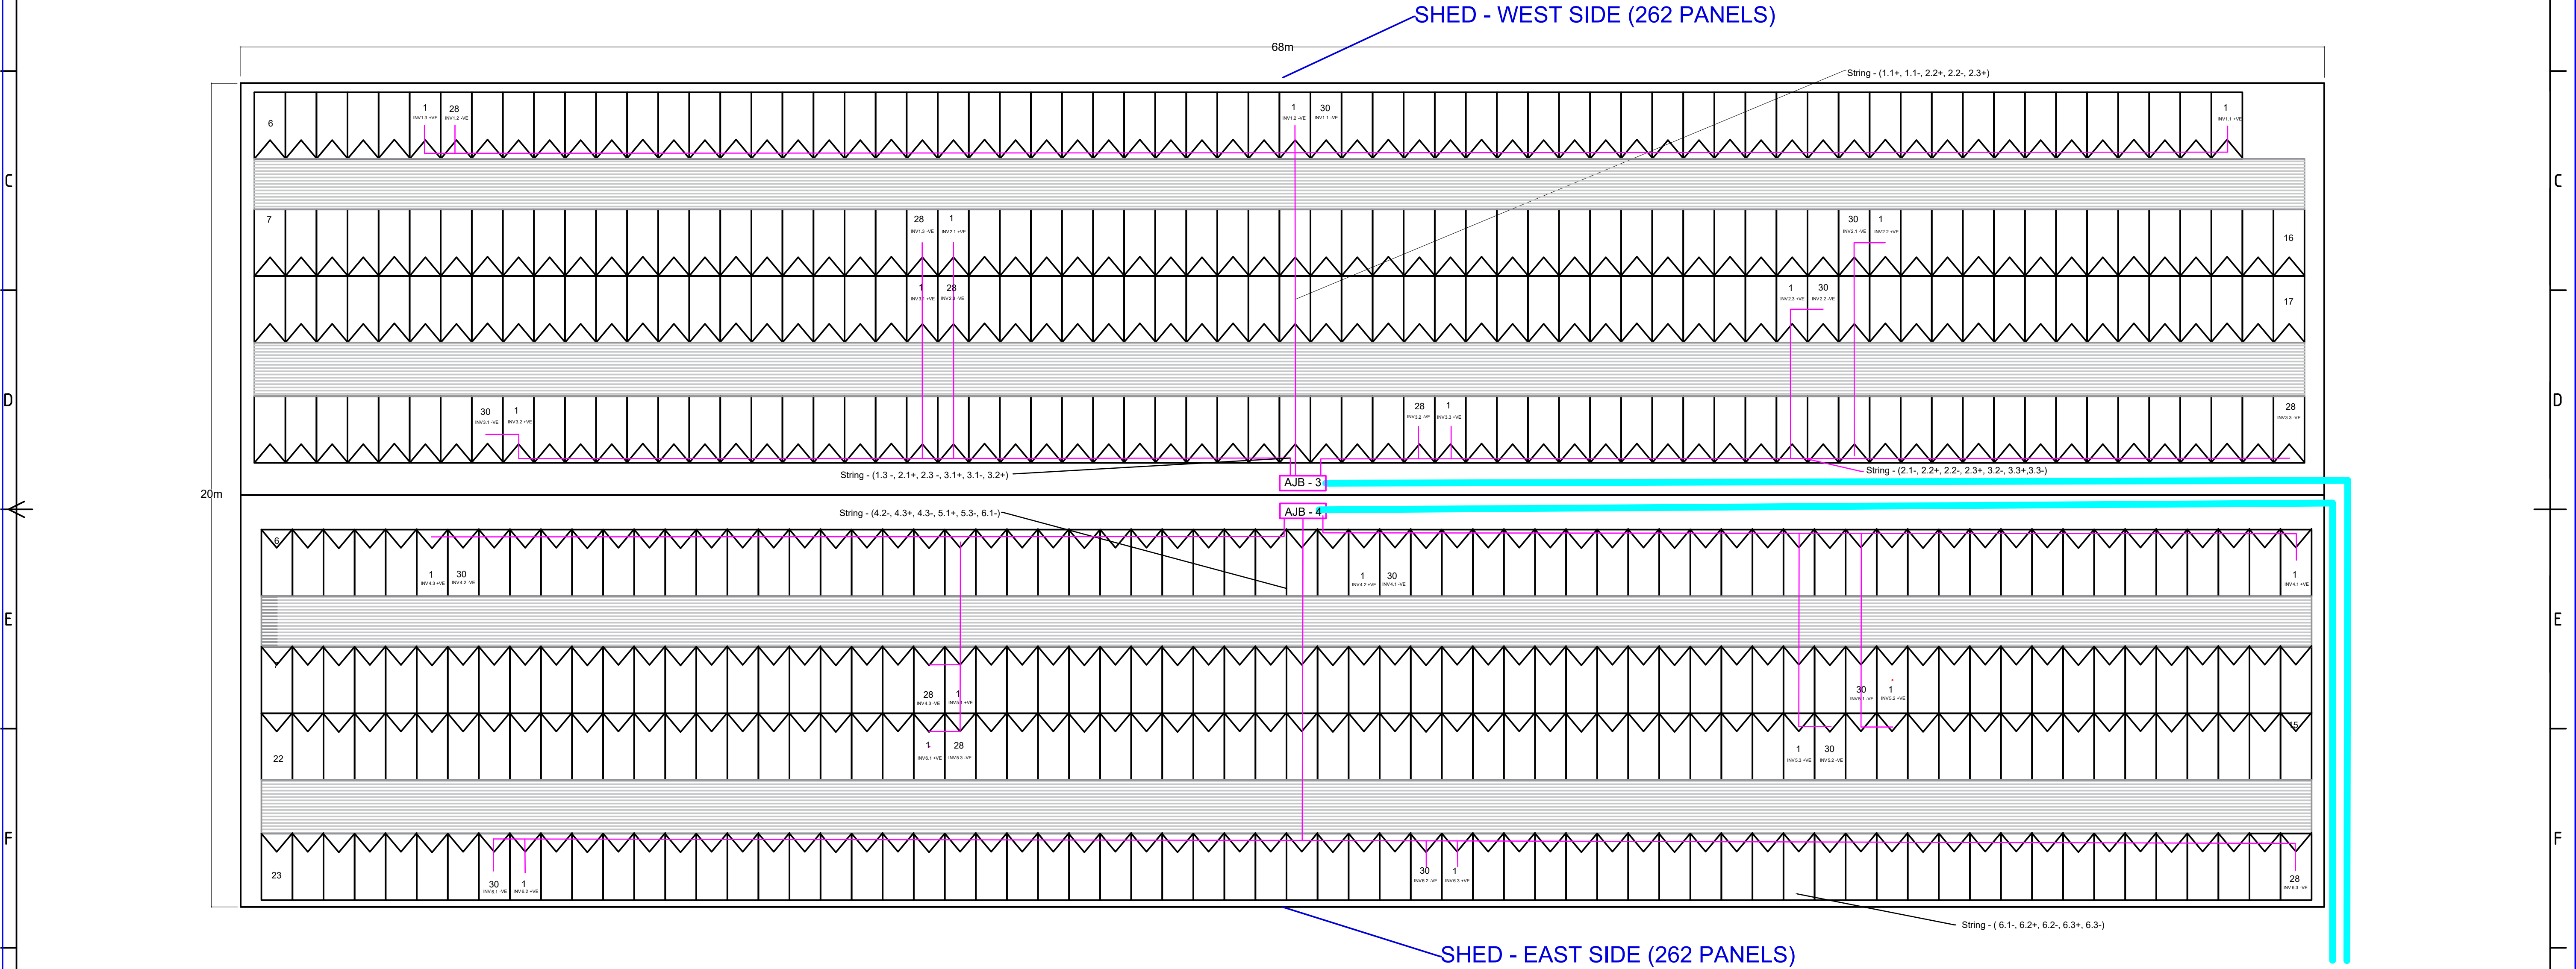

SYMBOL	DESCRIPTION
	CONDUIT LINING FROM PANEL TO AJB
	CONDUIT LINING FROM AJB TO INVERTER

237.4.2kwp on-Grid System - Mangomist Resort

Bangalore

Itemref	Quantity	Title/Name, designation, material, dimension etc			Article No./Reference	
Designed by Lakshmi	Checked by SC	Approved by - date SLC - 00/00/00	Filename EL-001	Date 2/12/2020	Scale N/A	
EcoSoch Solar Pvt Ltd				SINGLE LINE DIAGRAM		
DWG - EL - 001				Edition 0	Sheet 1/1	