
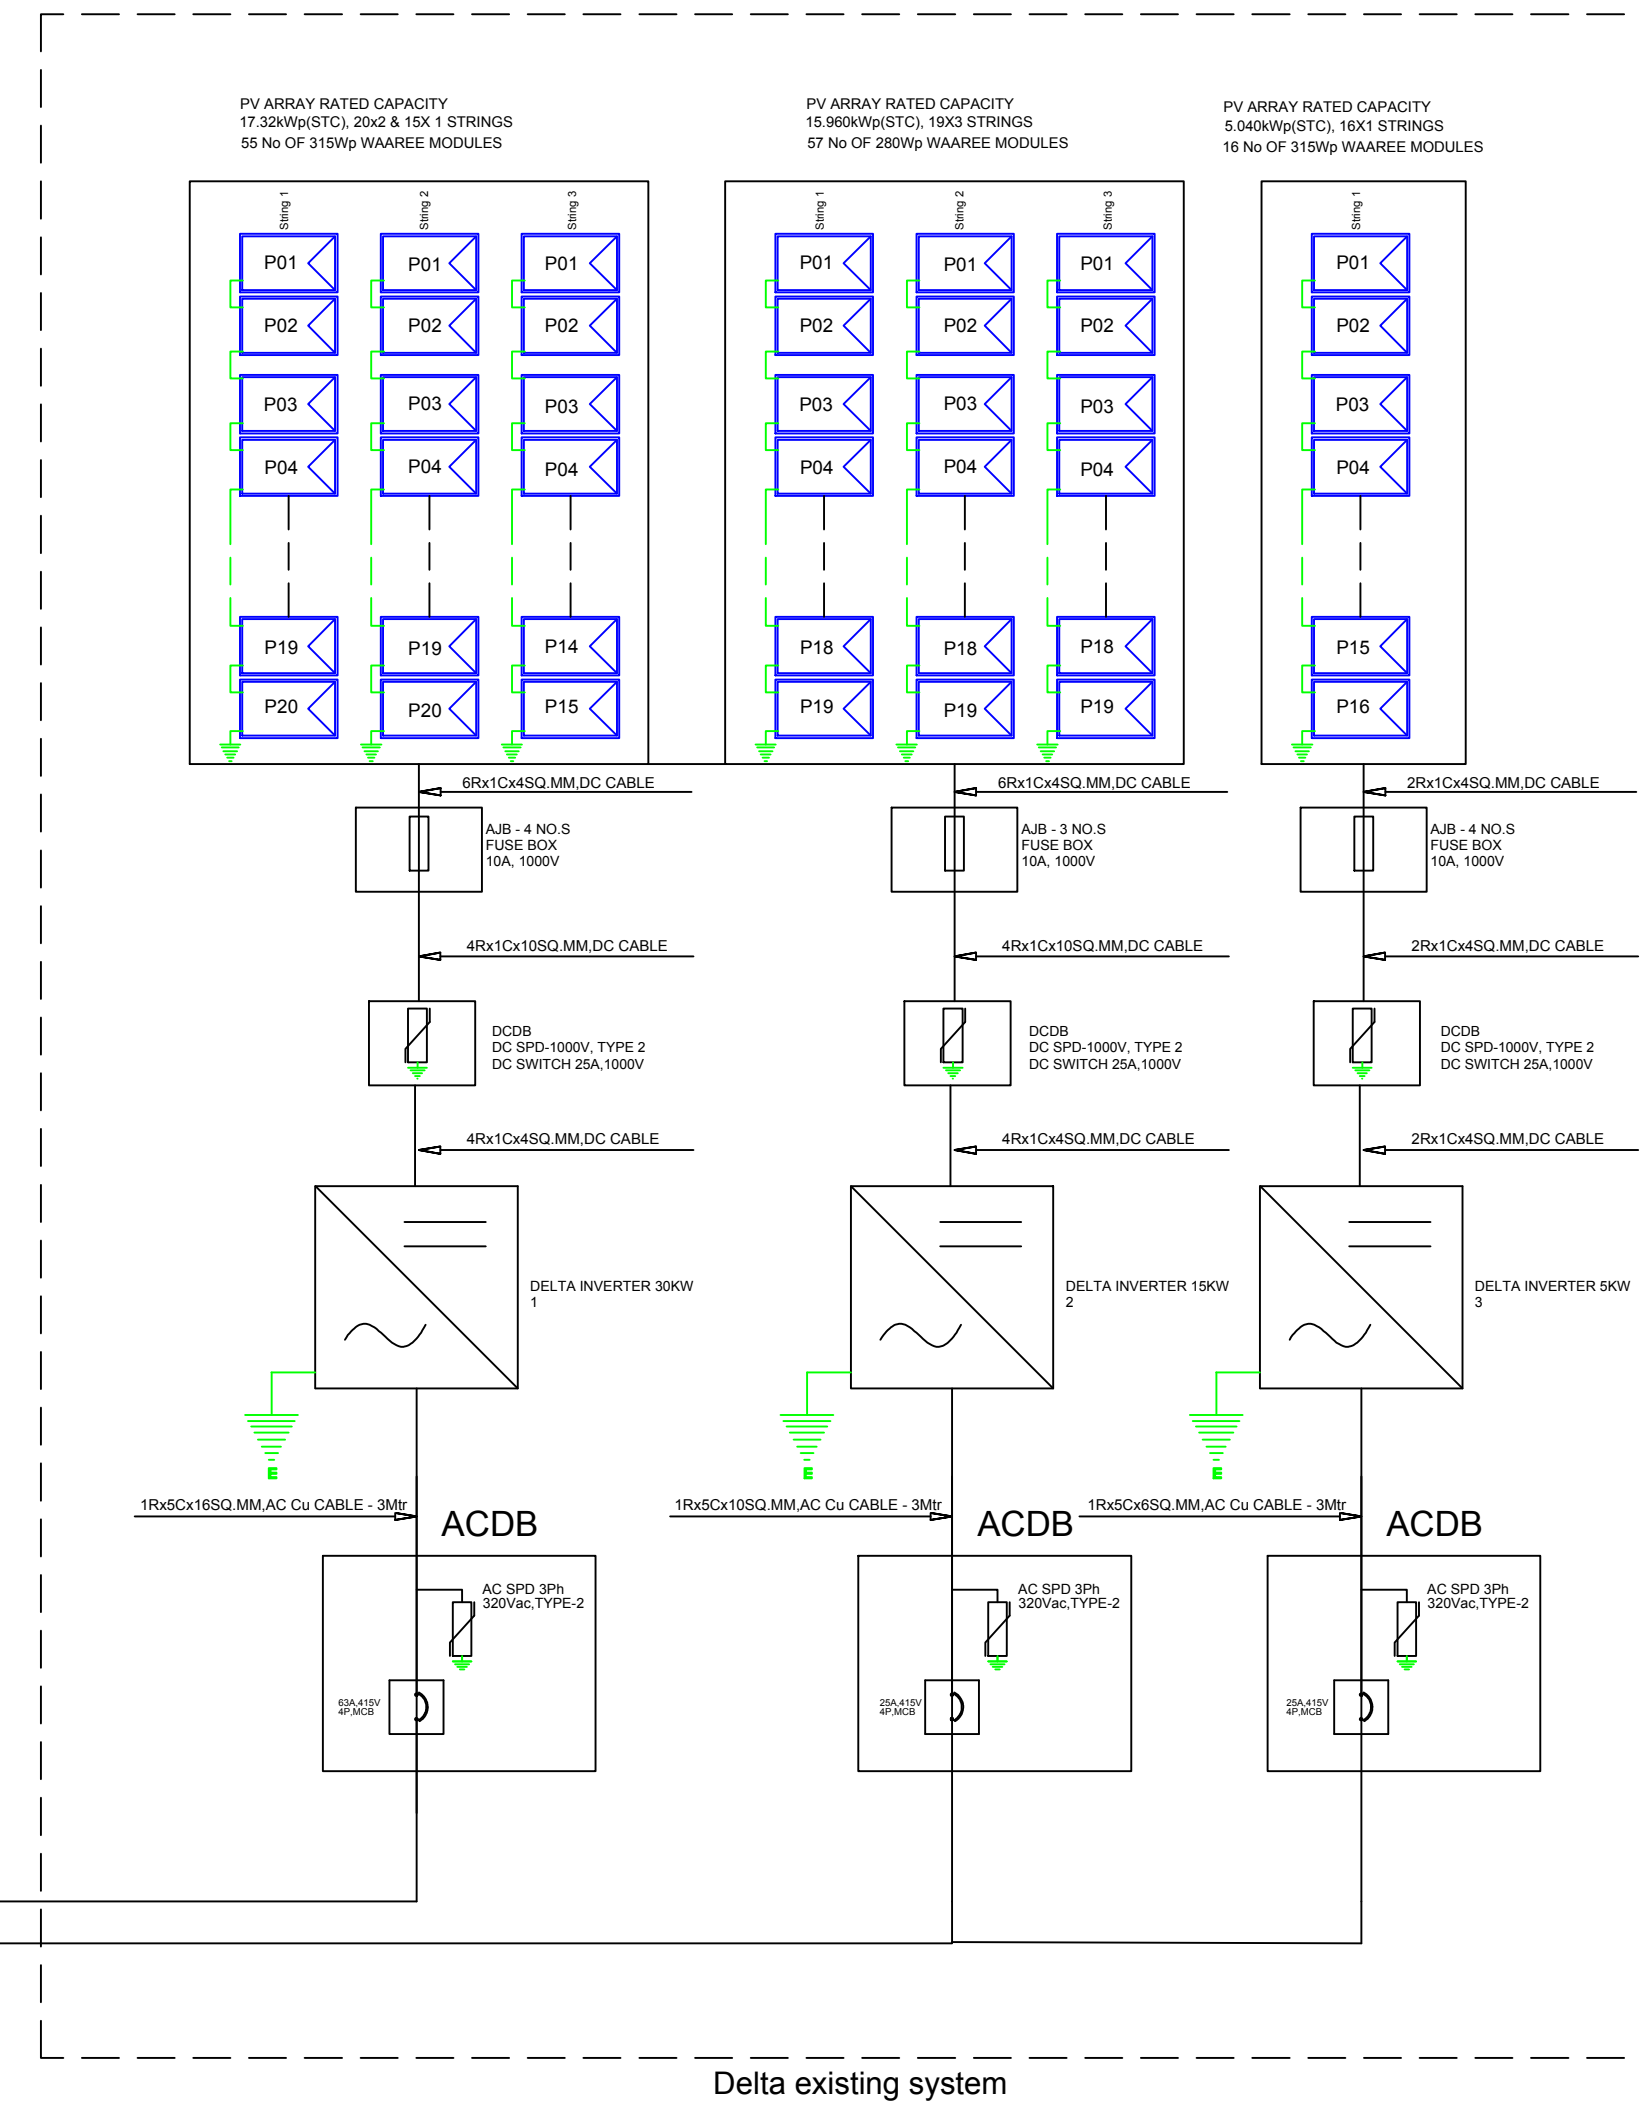


PROJECT INFORMATION

237.4kWp (DC) PHOTOVOLTAIC SYSTEM CONSISTING OF 654 WAAREE MODULES

38.32kWp (DC) PHOTOVOLTAIC SYSTEM

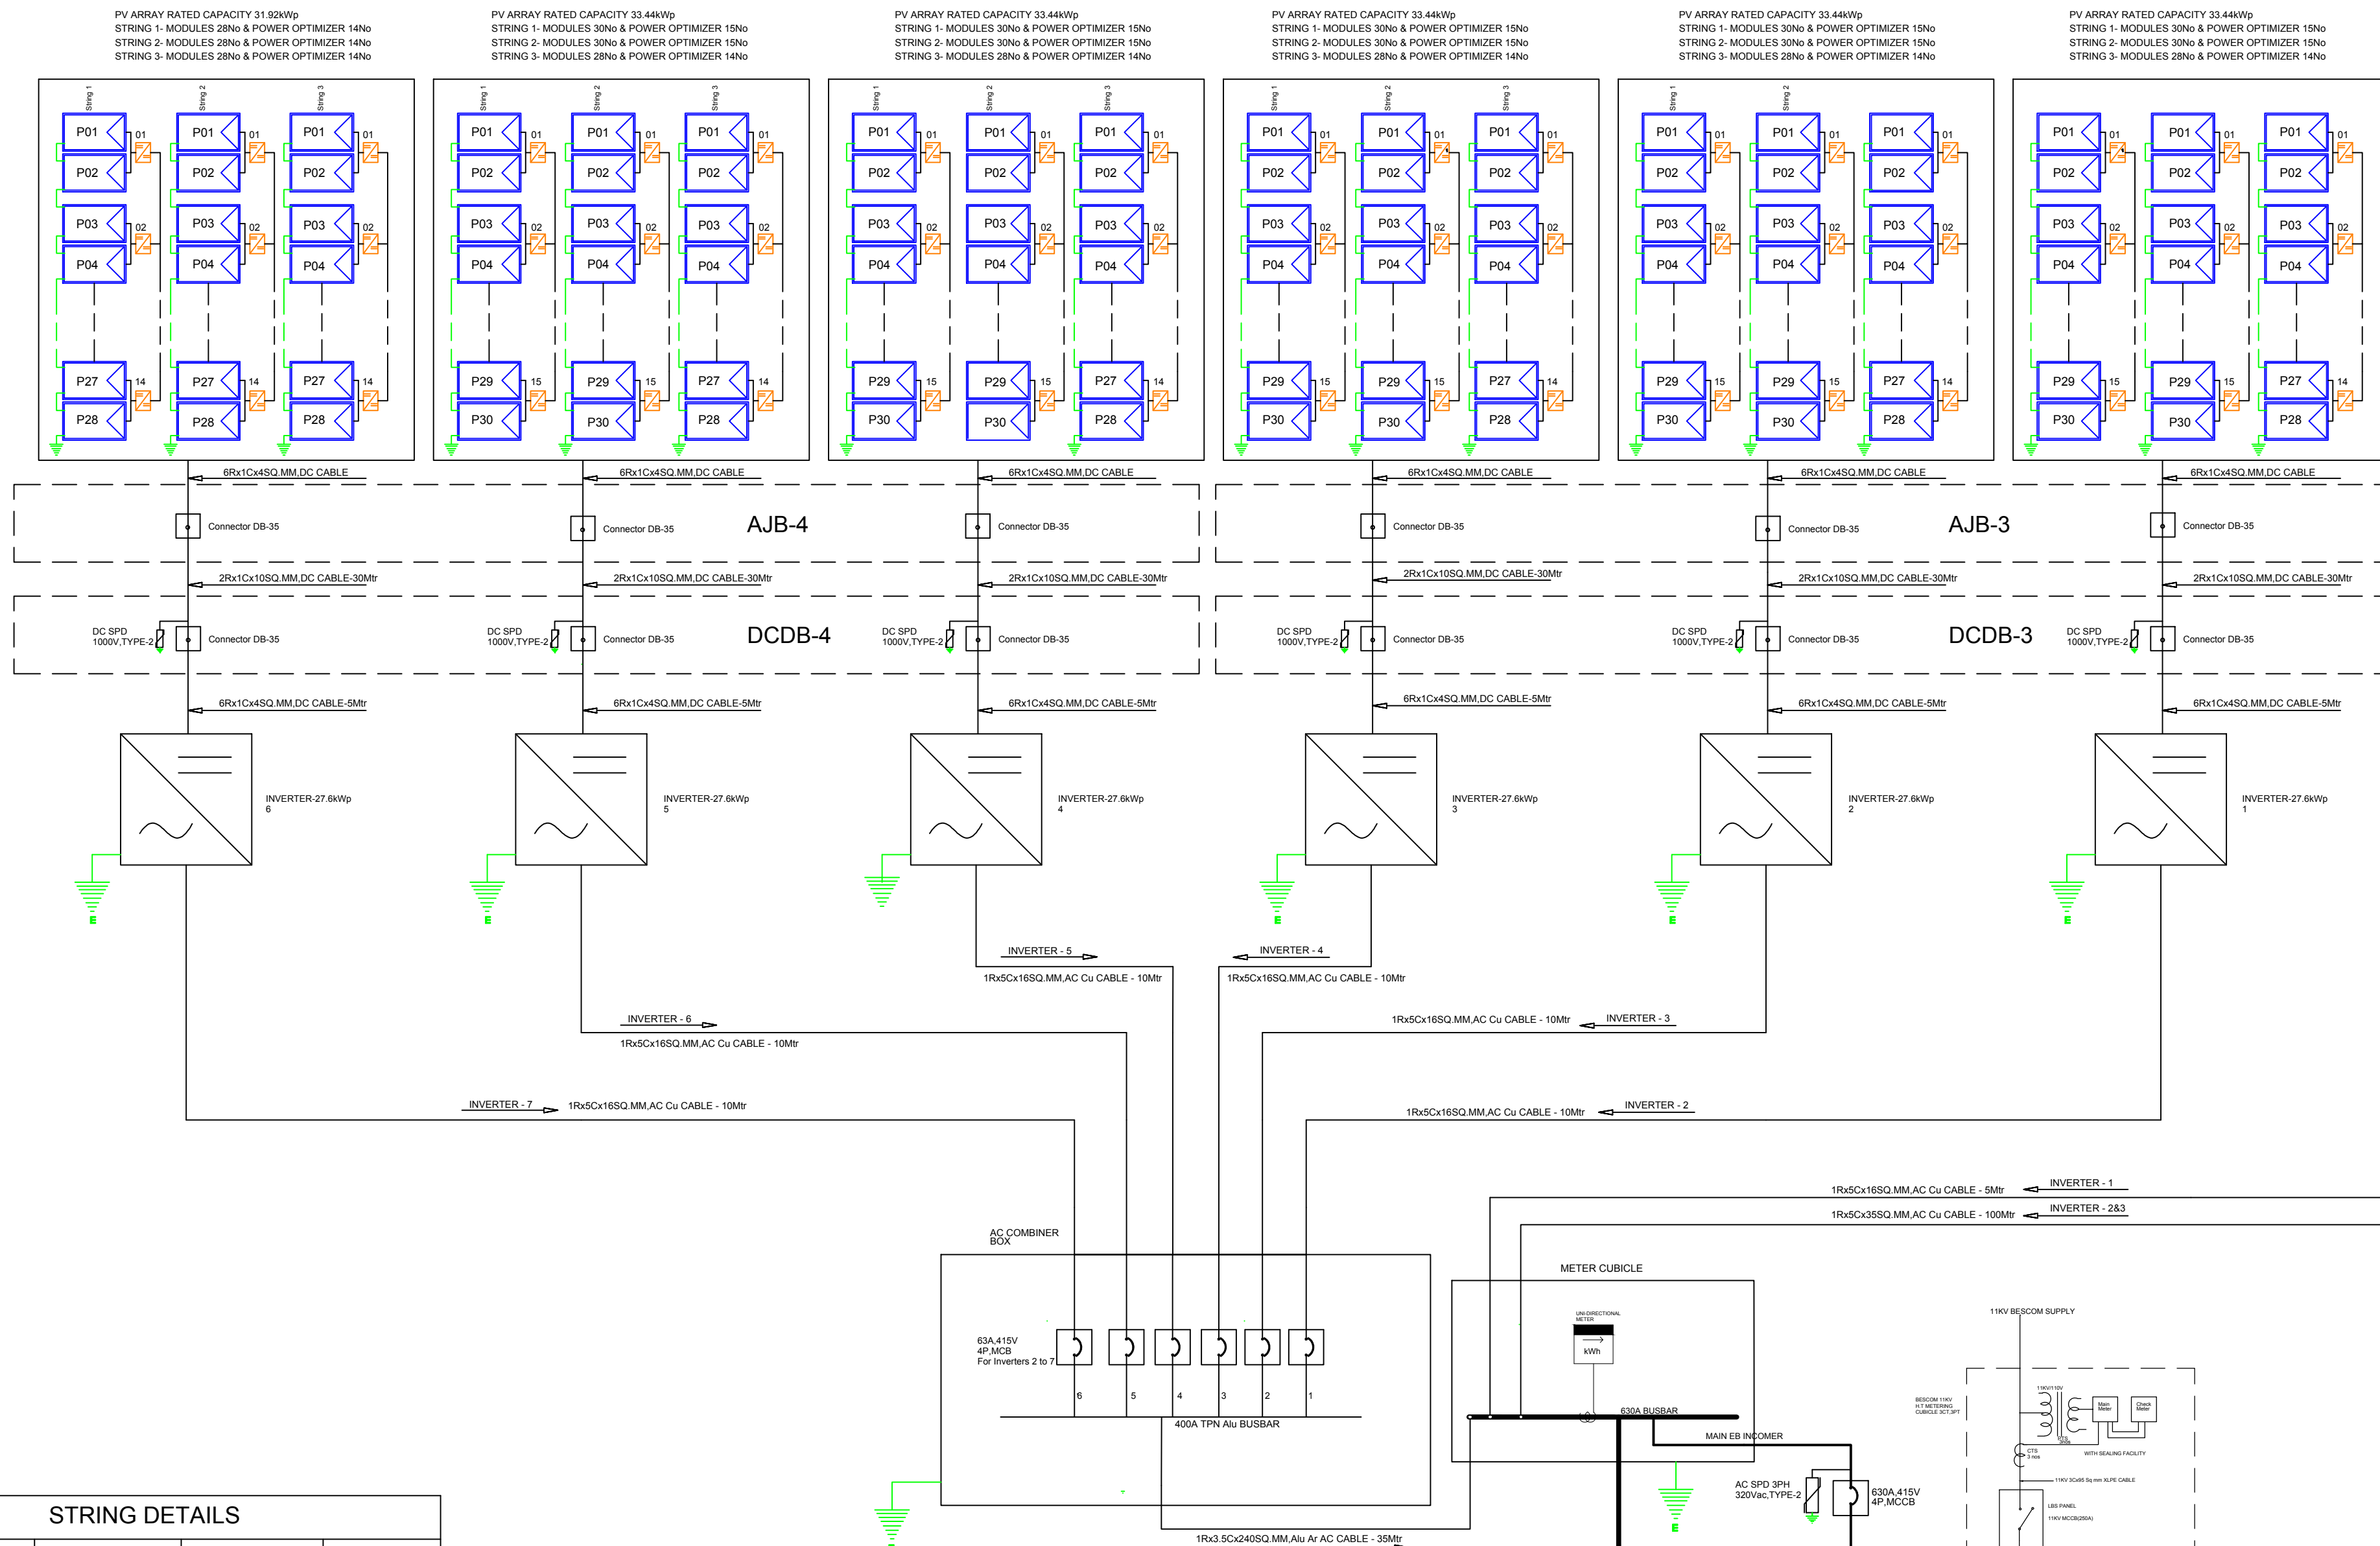

STRING DETAILS

INVERTER	STRING	MODULE	POWER OPTIMIZER
INVERTER-1	STRING-1	315W-20	NA
	STRING-2	315W-20	
	STRING-3	315W-15	
INVERTER-2	STRING-1	280W-19	NA
	STRING-2	280W-19	
	STRING-3	280W-19	
INVERTER-3	STRING-1	315W-16	NA
	STRING-2	315W-16	
	STRING-3	315W-16	
INVERTER-1 TO INVERTER-5	STRING-1	380W-30	P850-15 P850-15 P850-14
	STRING-2	380W-30	
	STRING-3	380W-28	
INVERTER-6	STRING-1	380W-28	P850-14 P850-14 P850-14
	STRING-2	380W-28	
	STRING-3	380W-28	

Legend

Symbol	Description
	PV Panel
	Power Optimizer
	SPD
	Inverter
	MCB
	MCCB
	Current Transformer
	Bi-Directional Meter
	Uni-Directional Meter

NOTE:

PLANT CAPACITY : 237.4kWp
TOTAL NUMBER OF MODULES : 654NOS
TOTAL NUMBER OF INVERTERS : 9
TOTAL NUMBER OF POWER OPTIMIZER : P850-262NOS,

SOLAREEDGE INVERTER-27.6KVA- 6 NO
DELTA INVERTER 30kVA - 1NO
DELTA INVERTER 15KVA - 1NO
DELTA INVERTER 5KVA - 1NO

POWER OPTIMIZER

OPTIMIZER MANUFACTURER : SOLAREEDGE P850
NO OF PANEL PER OPTIMIZER : 02 NOS

Itemref	Quantity	Title/Name, designation, material, dimension etc	Article No./Reference
Designed by Lakshmi	Checked by	Approved by - date	Filename EL - 001
Date 02/01/2020	Scale N/A	SINGLE LINE DIAGRAM	
ECO SOCH Sunny Living		DWG - EL - 001	Sheet 1/1