

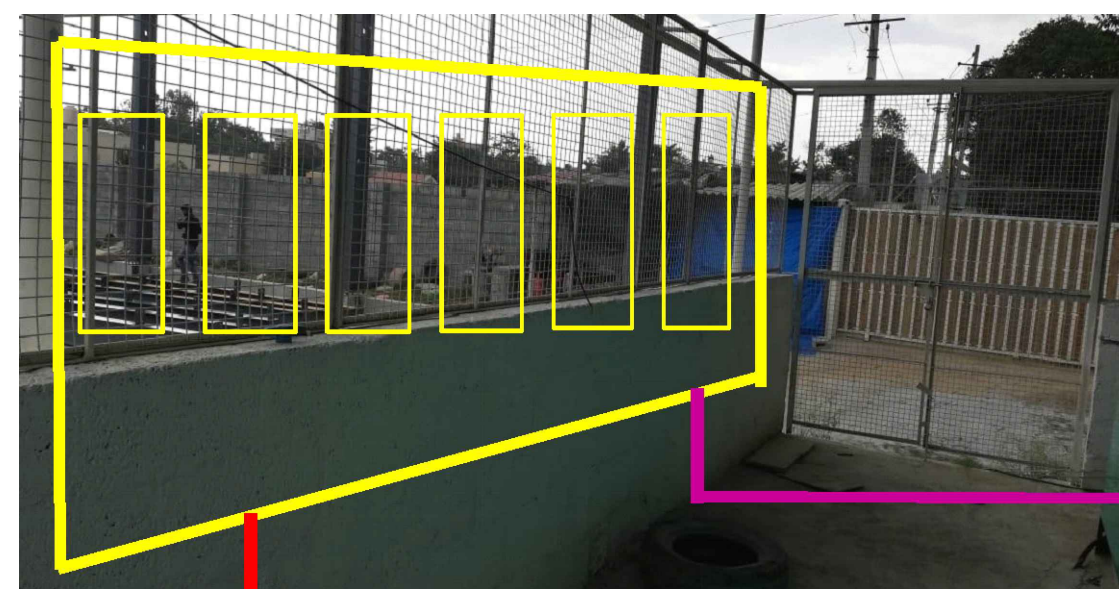


EQUIPMENT LAYOUT OF 199.88kWp SYSTEM

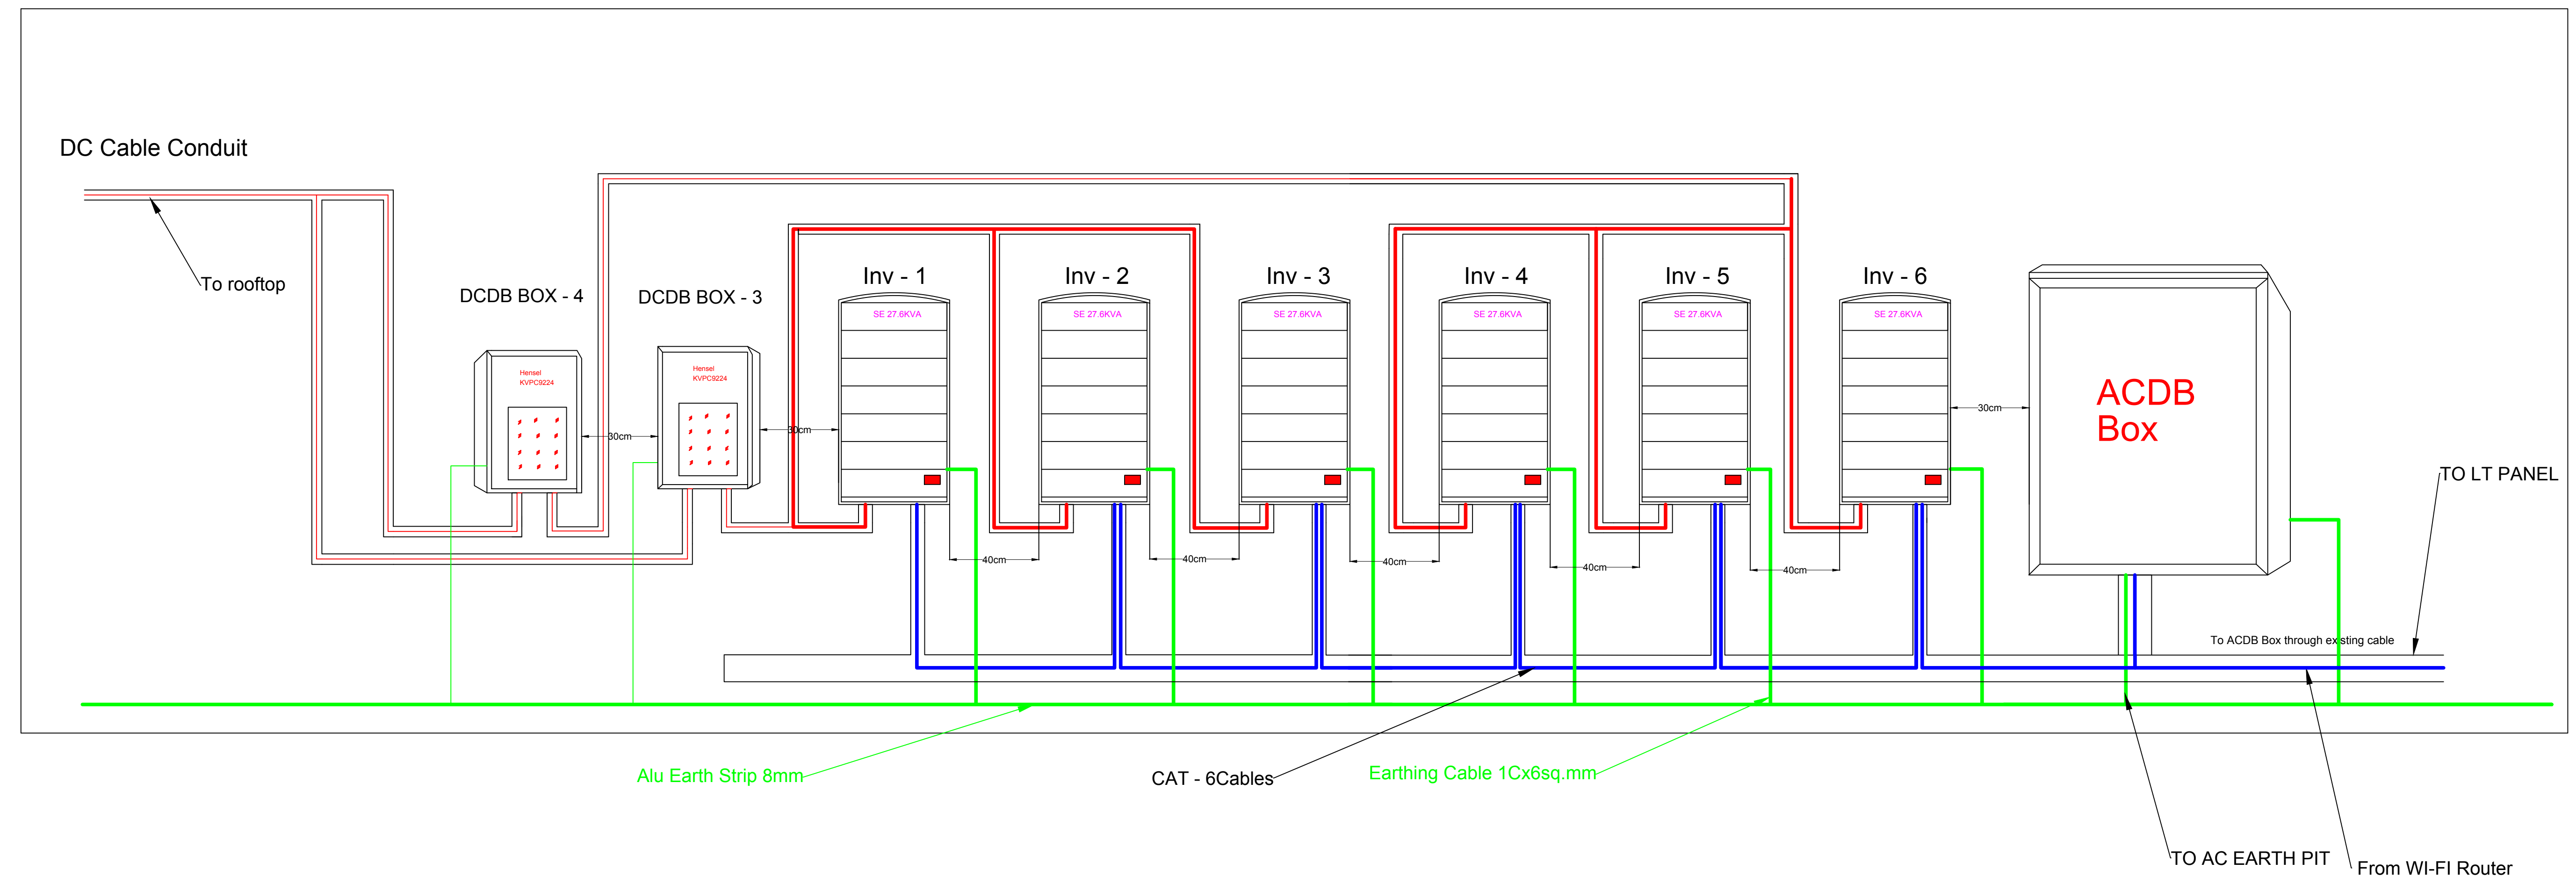


INVERTER LOCATION

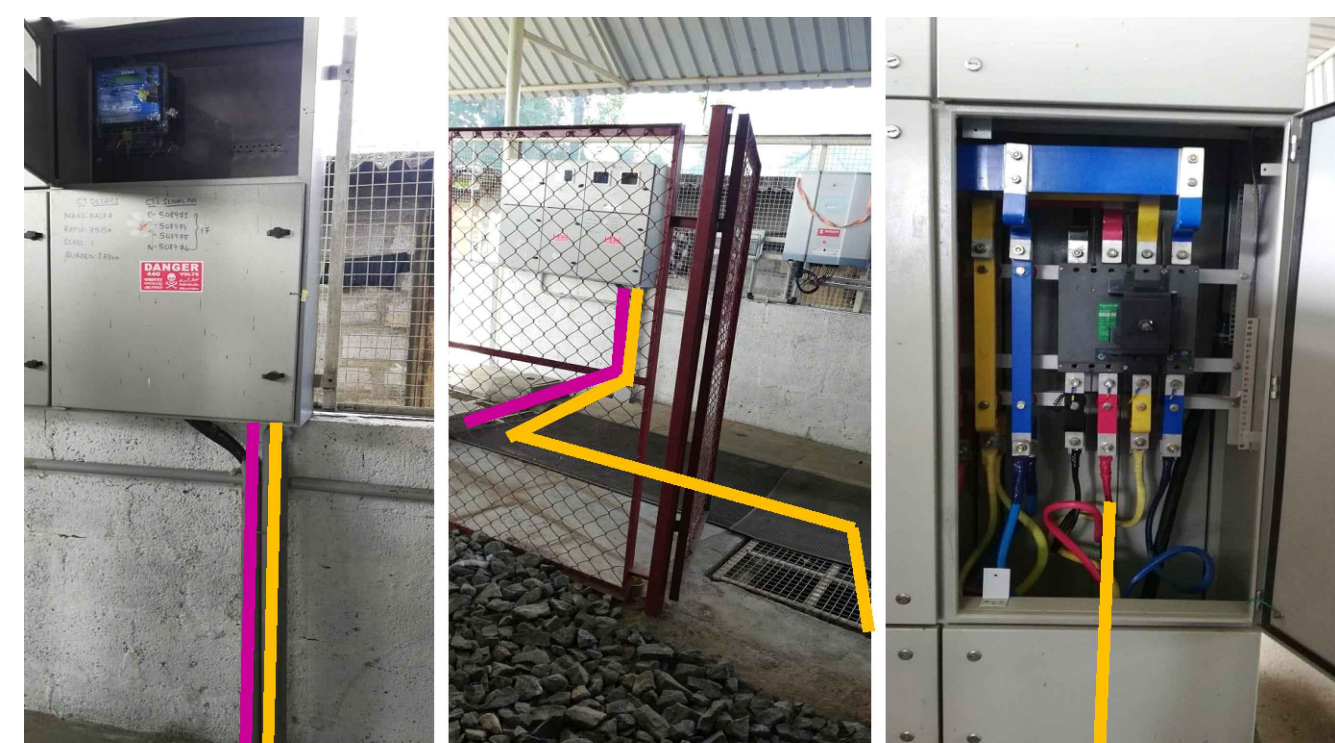

AC CABLE ROUTING FROM METER CUBICAL TO LT PANEL



AC CABLE ROUTING FROM INVERTER TO METER CUBICAL

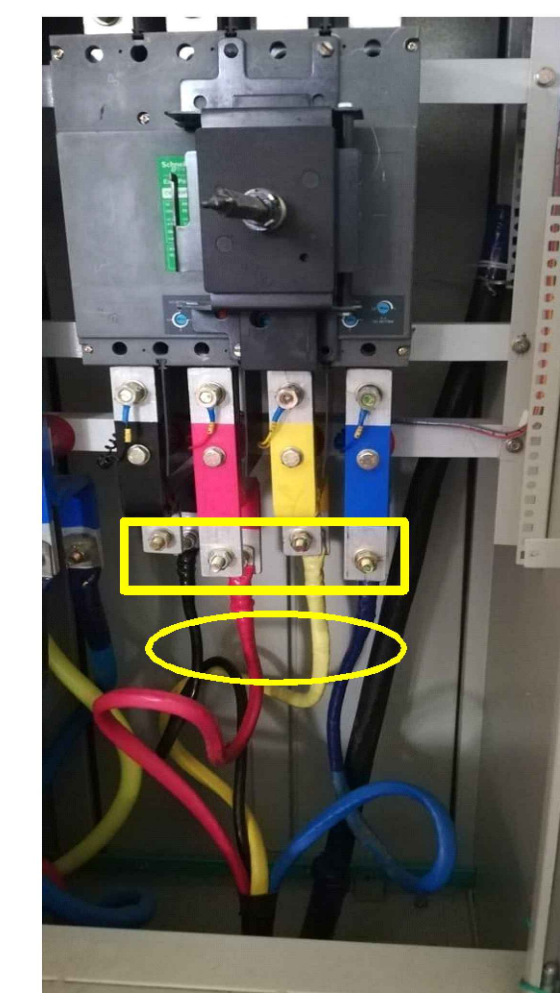

INTERCONNECTION POINT

Interconnection point

237.4kWp On - Grid system Mangomist Resort
Anekal Taluk, Bangalore.

Itemref	Quantity	Title/Name, designation, material, dimension etc			Article No./Reference	
Designed by Lakshmi	Checked by	Approved by - date	Filename EL - 004	Date 06/01/2020	Scale N/A	
EcoSoch Solar Pvt Ltd			EQUIPMENT MOUNTING LAYOUT			
DWG - EL - 004			Edition 03	Sheet 1/1		